اتجاه الشمال

قطعة رقم ٥٢

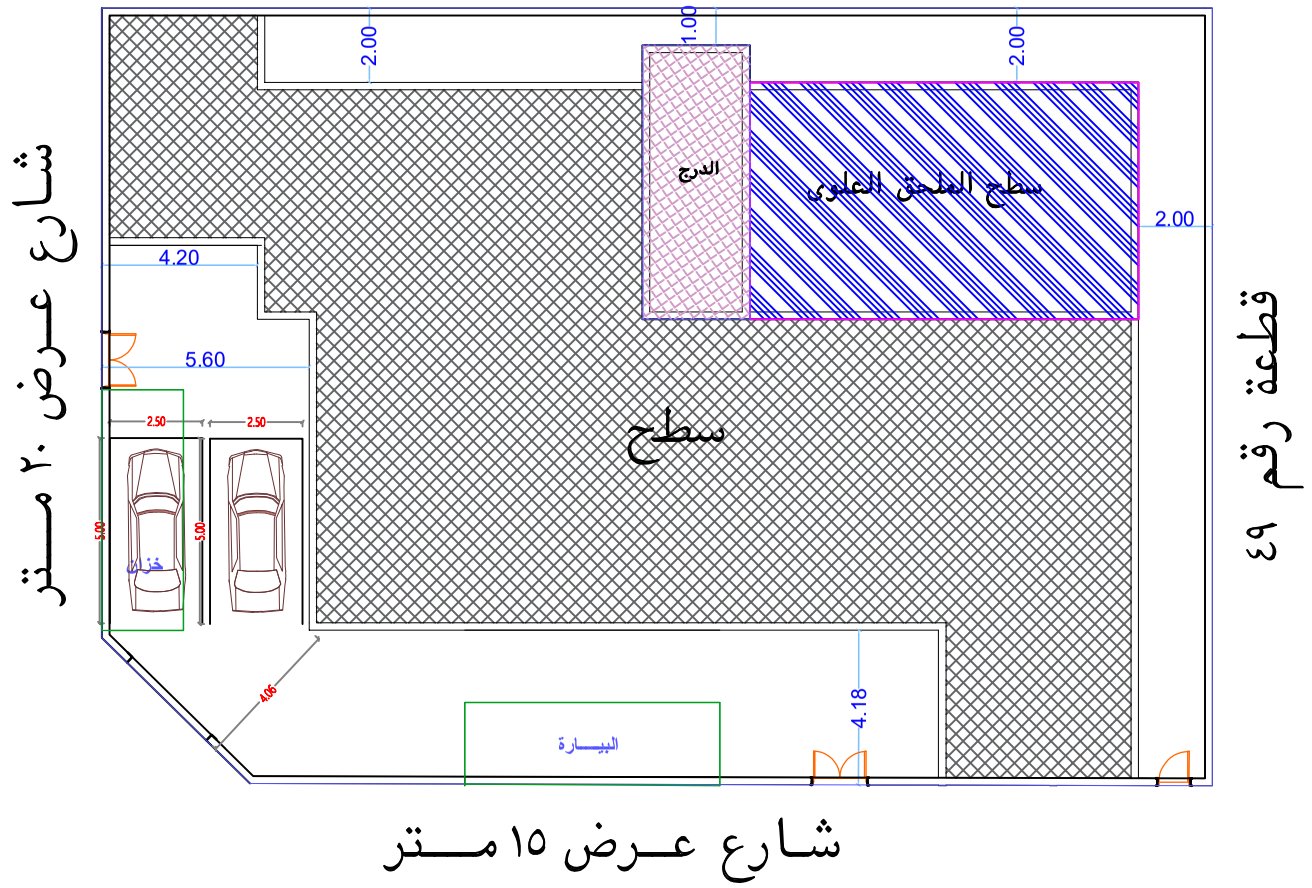

جدول مواقف	
الدور الارضى	١
الدور الاول	٠
الدور الثانى	٠
الدور الملحق علوى	١
اجمالى مواقف	٠

كمية الحفر
٤٥٠ م٣

حدود الارض
حدود الدورالارضي
الاول الدور حدود
البيارة و الخزان
حدود الدرج
حدود الملحق

الارتدادات

رقم	الجهة	الحدود	الطول	الارتداد	البروز
١	الشمال	قطعة رقم ٥٢	٣٠,٠٠م	٢٠,٠٠م	-
٢	الشرق	قطعة رقم ٤٩	٢١,٠٠م	٢,٠٠م	-
٣	الجنوب	شارع عرض ١٥ متر	٢٧,٠٠م	٤,١٨م	-
٤	الغرب	شارع عرض ٢٠ متر	١٨,٠٠م	٤,٢٠م	-

رقم	الوصف	المساحة	النسبة
١	المساحة الكلية	٦٢٥,٥ م٢	
٢	مساحة الدور الارضى بدون الملحق الارضى	-- م٢	-- ٪
٣	مساحة الملحق الارضى	-- م٢	-- ٪
٤	مساحة الدور الارضى كامل	٣٩٣,٢٨ م٢	٦٢,٨٧٪
٥	مساحة الدور الاول	-- م٢	-- ٪
٦	مساحة دور الملحق العلوى	٨٥,٨١ م٢	٧١,٨١٪ (دور الملحق العلوى)
٧	المساحة الاجمالية	٤٧٩,٠٩ م٢	

عدد الوحدات / ٢

عدد المواقف / ٢

اسم صاحب الرخصة	تركى محمد سويد العصيمى	رقم المخطط	١٧٩
رقم السجل المدنى	١٠٨٨١٤٢١٣٦	رقم الصك	٦١٠٥٠٨٠٠٢٢٩١
اسم المشروع	فيلا سكنية	قطعة رقم	٥٠
اسم اللوحة	الموقع العام	الحى	طحى
مقياس الرسم	١/١٠٠	نوع المخطط	سكنى

بيانات خاصة بالموقع

الموقع	بلدية الرويضه		اتجاه الشمال
المنطقة	الرياض / طحى		
رقم القطعة	٥٠	رقم المخطط	١٧٩ الواقع بطحى
رقم الصك	٦١٠٥٠٨٠٠٢٢٩١	تاريخ الصك	١٤٤٦/١١/٣هـ
مساحة الارض بموجب التقرير المساحى	٦٢٥,٥ م٢	رقم اللوحة الجوية	
مساحة الارض بموجب التنظيم	٦٢٥,٥ م٢	مساحة الارض بموجب الطبيعة	٦٢٥,٥م٢

2030

أمانة منطقة الرياض
RIYADH REGION MUNICIPALITY

ملاحظة:

- تم مراعاة تطبيق كود البناء السعودى فى تصميم المشروع
-(يعتمد على مسئولية المكتب الهندسى و متوافق مع كود البناء السعودى و مع الأنظمة و اللوائح المعتمدة التى تتطلبها وزارة النقل و الادارة العامة للدفاع المدنى ووزارة المياه و الكهرباء)
- تم اعداد مخططات العزل الحرارى للمبنى وفق متطلبات العزل الحرارى الواردةفى كود البناء السعودى

مكتب أحمد عبدالله العصيمي للاستشارات الهندسية
AHMED ABDULLAH ALOSAIMI
ENGINEERING CONSULTANT
ترخيص رقم : 5100003773
shg

PROJECT: اسم المشروع : عمارة سكنية

LOCATION: الموقع : طحى

OWNER: المالك: تركى محمد ابن سويد العصيمى

المهندس الانشائى: احمدعبدالله العصيمى
عضوية هيئة المهندسين: رقم ٢٦٣٧٣١

المهندس المعمارى: مصطفى يوسف محمد احمد
عضوية هيئة المهندسين: رقم ٣٨٩٩٣٩

DRAWING OF: اسم اللوحة: الموقع العام

مقياس الرسم: SCALE: 1:100
رقم اللوحة: DWG.N ٠٣
التاريخ: DATE: ٢٨-٤-٢٠٢٥م

اعتماد المكتب:

اتجاه الشمال

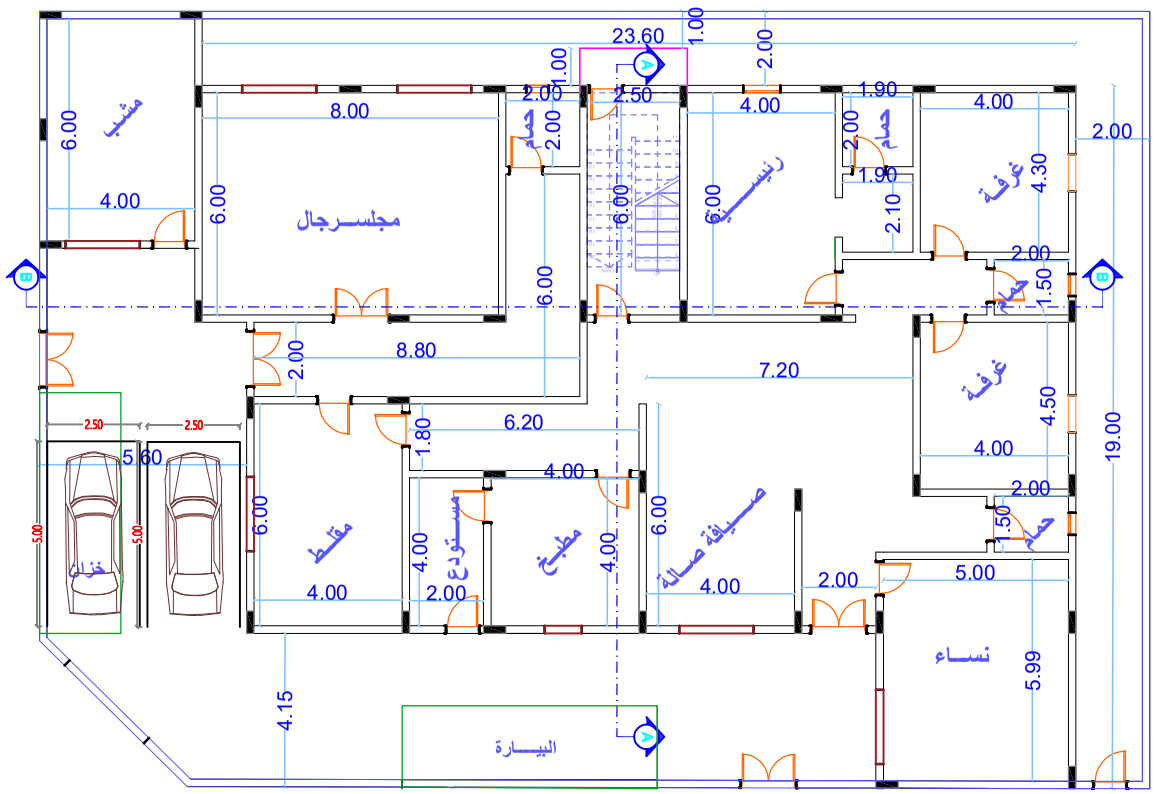

مسقط الدور الارضى

جدول مواقف

الدور الارضى	١
الدور الاول	٠
الدور الثانى	٠
الدور الملحق علوى	١
اجمالى مواقف	٠

كمية الحفر

٤٥٠ م٣

جدول الابواب

الموديل	المقاسات عرض	ارتفاع	جلسة	المواصفات
ب ١	٠,٩٠	٢,١٠	--	حسب الطلب
ب ٢	١,٠٠	٢,١٠	--	
ب ٣	١,٢٠	٢,٤٠	--	
ب ٤	١,٢٠	٢,١٠	--	
ب ٥	١,٥٠	١,٤٠		
ب ٦				
ب ٧				
ب ٨				
ب ٩				

جميع مقاسات الابواب صافى بعد الحلق والبلاط

جدول الشبابيك

الموديل	المقاسات عرض	ارتفاع	جلسة	المواصفات
ش ١	١,٥٠	٢,٠٠	١,٠٠	
ش ٢	١,٢٢	٢,٠٠	١,٠٠	حسب الطلب
ش ٣	,٦٠	,٦٠	٢,٠٠	
ش ٤				
ش ٥				
ش ٦				
ش ٧				
ش ٨				
ش ٩				
ش ١٠	حسب الشكل فى الواجهة وطلب المالك خلال التنفيذ			

تشطيبات الارضيات	
باركيه	
رخام	
بورسلين	
بلاط بورسلين	
سيراميك	
بلاط	
عشب	

بيانات خاصة بالموقع

الموقع	بلدية الرويضه		اتجاه الشمال
المنطقة	الرياض / طحى		
رقم القطعة	٥٠	رقم المخطط	١٧٩ الواقع بطحى
رقم الصك	٦١٠٥٠٨٠٠٢٢٩١	تاريخ الصك	١٤٤٦/١١/٣هـ
مساحة الارض بموجب التقرير المساحى	٦٢٥,٥ م٢	رقم اللوحة الجوية	
مساحة الارض بموجب التنظيم	٦٢٥,٥ م٢	مساحة الارض بموجب الطبيعة	٦٢٥,٥م٢

2030

أمانة منطقة الرياض
RIYADH REGION MUNICIPALITY

ملاحظة:

- تم مراعاة تطبيق كود البناء السعودى فى تصميم المشروع
-(يعتمد على مسئولية المكتب الهندسى و متوافق مع كود البناء السعودى و مع الأنظمة و اللوائح المعتمدة التى تتطلبها وزارة النقل و الادارة العامة للدفاع المدنى ووزارة المياه و الكهرباء)
- تم اعداد مخططات العزل الحرارى للمبنى وفق متطلبات العزل الحرارى الواردةفى كود البناء السعودى

مكتب أحمد عبدالله العصيمي للاستشارات الهندسية
AHMED ABDULLAH ALOSAIMI
ENGINEERING CONSULTANT
ترخيص رقم : 5100003773

PROJECT: اسم المشروع : عمارة سكنية

LOCATION: الموقع : طحى

OWNER: المالك: تركى محمد ابن سويد العصيمى

المهندس الانشائى: احمدعبدالله العصيمى
عضوية هيئة المهندسين: رقم ٢٦٣٧٣١

المهندس المعمارى: مصطفى يوسف محمد احمد
عضوية هيئة المهندسين: رقم ٣٨٩٩٣٩

DRAWING OF: اسم اللوحة: مسقط الدور الارضى

مقياس الرسم: SCALE: 1:100
رقم اللوحة: DWG.N ٠٣
التاريخ : DATE: ٢٨-٤-٢٠٢٥م

اعتماد المكتب:

اتجاه الشمال

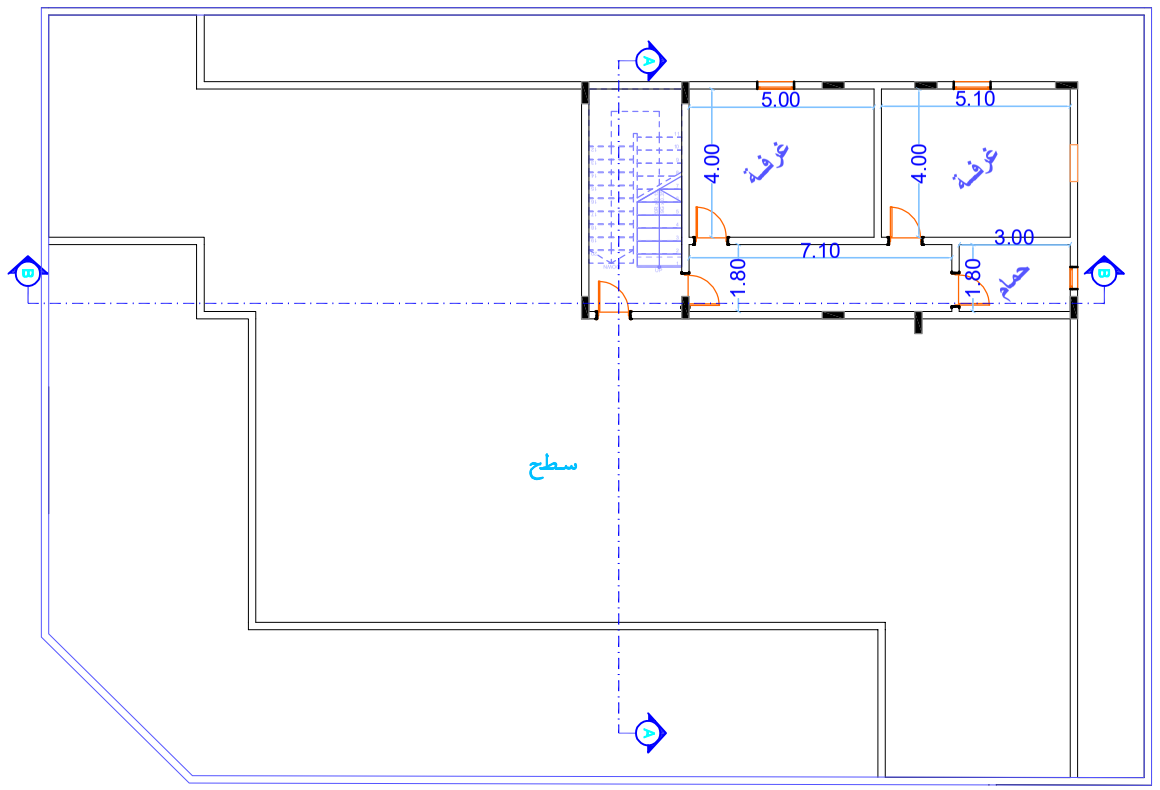

مسقط افقى للدور الملحق

بيانات خاصة بالموقع

الموقـــع	بلدية الرويضه		اتجاه الشمال
المنطقـــة	الرياض / طحى		
رقـــم القطعـــة	٥٠	رقم المخطط	١٧٩ الواقع بطحى
رقـــم الصـــك	٦١٠٥٠٨٠٠٢٢٩١	تاريـــخ الصـــك	١٤٤٦/١١/٣هـ
مساحة الارض بموجب التقرير المساحى	٦٢٥,٥ م٢	رقـم اللوحة الجوية	
مساحة الارض بموجب التنظيم	٦٢٥,٥ م٢	مساحة الارض بموجب الطبيعة	٦٢٥,٥م٢

2030

أمانة منطقة الرياض
RIYADH REGION MUNICIPALITY

ملاحظة:

- تم مراعاة تطبيق كود البناء السعودى فى تصميم المشروع
-(يعتمد على مسئولية المكتب الهندسى و متوافق مع كود البناء السعودى و مع الأنظمة و اللوائح المعتمدة التى تتطلبها وزارة النقل و الادارة العامة للدفاع المدنى ووزارة المياه و الكهرباء)
- تم اعداد مخططات العزل الحرارى للمبنى وفق متطلبات العزل الحرارى الواردةفى كود البناء السعودى

مكتب أحمد عبدالله العصيمي للاستشارات الهندسية
AHMED ABDULLAH ALOSAIMI
ENGINEERING CONSULTANT
ترخيص رقم : 5100003773
shg

PROJECT: اسم المشروع : عمارة سكنية

LOCATION: الموقع : طحى

OWNER: المالك: تركى محمد ابن سويد العصيمى

المهندس الانشائى: احمدعبدالله العصيمى
عضوية هيئة المهندسين: رقم ٣٦٣٧٣١

المهندس المعمارى: مصطفى يوسف محمد احمد
عضوية هيئة المهندسين: رقم ٣٨٩٩٣٩

DRAWING OF: اسم اللوحة: مسقط افقى للدور الملحق

مقياس الرسم: SCALE: 1:100
رقم اللوحة: DWG.N ٠٣
اعتماد المكتب:

DATE: التاريخ : ٢٨-٤-٢٠٢٥م

اتجاه الشمال

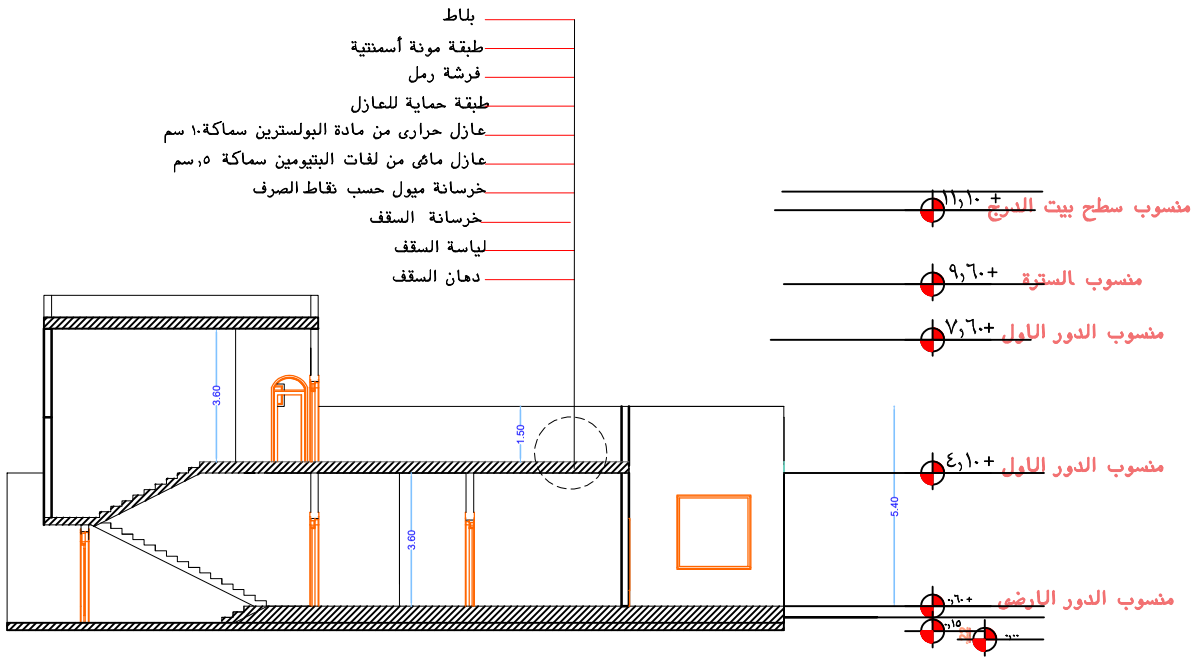

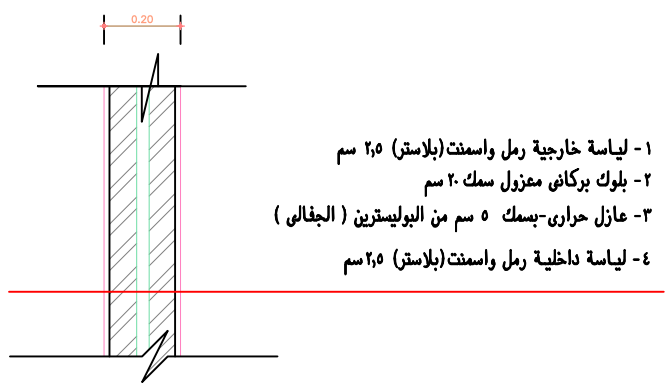

قطاع تفصيلى لعزل الحوائط الخارجية

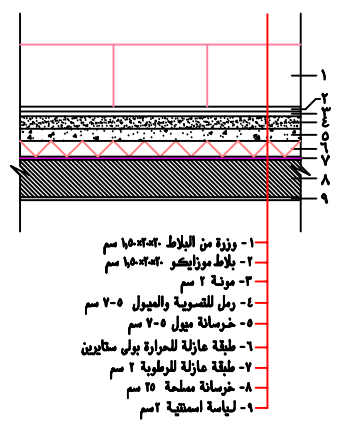

قطاع تفصيلى لعزل الاسقف

بيانات خاصة بالموقع

الموقـــع	بلدية الرويضه		اتجاه الشمال
المنطقـــة	الرياض / طحى		
رقـــم القطعـــة	٥٠	رقم المخطط	١٧٩ الواقع بطحى
رقـــم الصـــك	٦١٠٥٠٨٠٠٢٢٩١	تاريـــخ الصـــك	١٤٤٦/١١/٣هـ
مساحة الارض بموجب التقرير المساحى	٦٢٥,٥ م٢	رقـم اللوحة الجوية	
مساحة الارض بموجب التنظيم	٦٢٥,٥ م٢	مساحة الارض بموجب الطبيعة	٦٢٥,٥م٢

2030

أمانة منطقة الرياض
RIYADH REGION MUNICIPALITY

ملاحظة:

- تم مراعاة تطبيق كود البناء السعودى فى تصميم المشروع
-(يعتمد على مسئولية المكتب الهندسى و متوافق مع كود البناء السعودى و مع الأنظمة و اللوائح المعتمدة التى تتطلبها وزارة النقل و الادارة العامة للدفاع المدنى ووزارة المياه و الكهرباء)
- تم اعداد مخططات العزل الحرارى للمبنى وفق متطلبات العزل الحرارى الواردةفى كود البناء السعودى

مكتب أحمد عبدالله العصيمي للاستشارات الهندسية
AHMED ABDULLAH ALOSAIMI
ENGINEERING CONSULTANT
ترخيص رقم : 5100003773

PROJECT: اسم المشروع : عمارة سكنية

LOCATION: الموقع : طحى

OWNER: المالك: تركى محمد ابن سويد العصيمى

المهندس الانشائى: احمدعبدالله العصيمى — عضوية هيئة المهندسين: رقم ٣٦٣٧٣١

المهندس المعمارى: مصطفى يوسف محمد احمد — عضوية هيئة المهندسين: رقم ٣٨٩٩٣٩

DRAWING OF: اسم اللوحة: مسقط راسى ا

مقياس الرسم: SCALE: 1:100 — رقم اللوحة: DWG.N ٠٣ — اعتماد المكتب:

DATE: التاريخ : ٢٨-٤-٢٠٢٥م

اتجاه الشمال

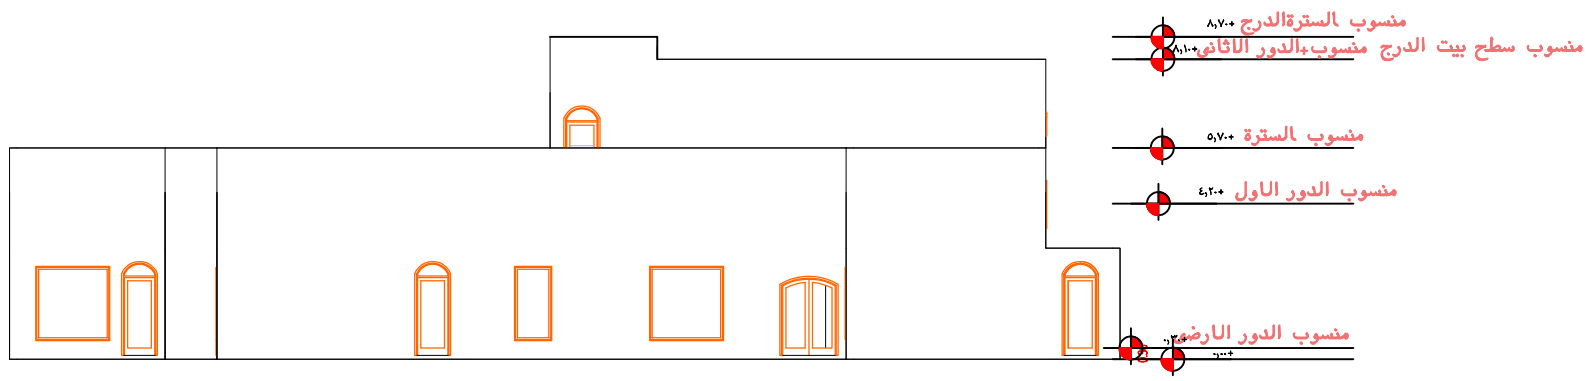

واجهة شمالية

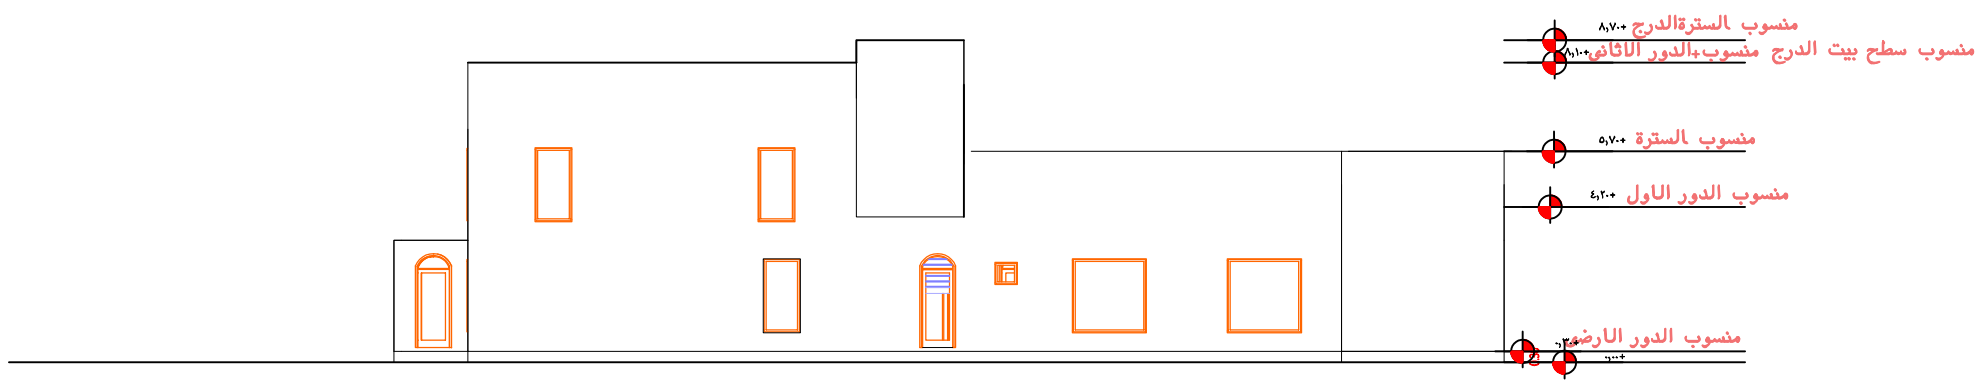

واجهة جنوبية

بيانات خاصة بالموقع

الموقـــع	بلدية الرويضه		اتجاه الشمال
المنطقـــة	الرياض / طحى		
رقـــم القطعـــة	٥٠	رقم المخطط	١٧٩ الواقع بطحى
رقـــم الصـــك	٦١٠٥٠٨٠٠٢٢٩١	تاريـــخ الصـــك	١٤٤٦/١١/٣هـ
مساحة الارض بموجب التقرير المساحى	٦٢٥,٥ م٢	رقـم اللوحة الجوية	
مساحة الارض بموجب التنظيم	٦٢٥,٥ م٢	مساحة الارض بموجب الطبيعة	٦٢٥,٥م٢

2030

أمانة منطقة الرياض
RIYADH REGION MUNICIPALITY

ملاحظة:

- تم مراعاة تطبيق كود البناء السعودى فى تصميم المشروع
-(يعتمد على مسئولية المكتب الهندسى و متوافق مع كود البناء السعودى و مع الأنظمة و اللوائح المعتمدة التى تتطلبها وزارة النقل و الادارة العامة للدفاع المدنى ووزارة المياه و الكهرباء)
- تم اعداد مخططات العزل الحرارى للمبنى وفق متطلبات العزل الحرارى الواردةفى كود البناء السعودى

مكتب أحمد عبدالله العصيمي للاستشارات الهندسية
AHMED ABDULLAH ALOSAIMI
ENGINEERING CONSULTANT
ترخيص رقم : 5100003773
shg

PROJECT: اسم المشروع : عمارة سكنية

LOCATION: الموقع : طحى

OWNER: المالك: تركى محمد ابن سويد العصيمى

المهندس الانشائى: احمدعبدالله العصيمى
عضوية هيئة المهندسين: رقم ٢٦٣٧٣١

المهندس المعمارى: مصطفى يوسف محمد احمد
عضوية هيئة المهندسين: رقم ٣٨٩٩٣٩

DRAWING OF: اسم اللوحة: الواجهات

مقياس الرسم: SCALE: 1:100

رقم اللوحة: DWG.N ٠٣

التاريخ : DATE: ٢٨-٤-٢٠٢٥م

اعتماد المكتب:

اتجاه الشمال

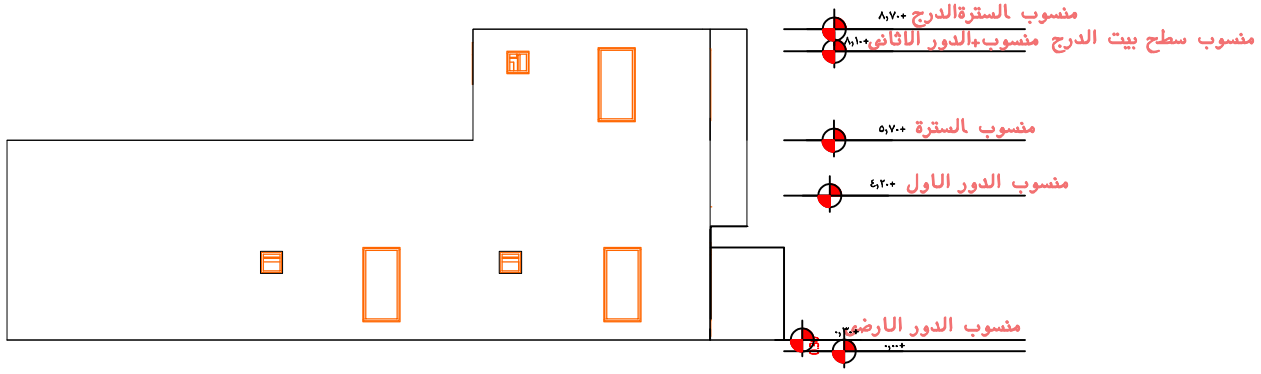

واجهة غربية

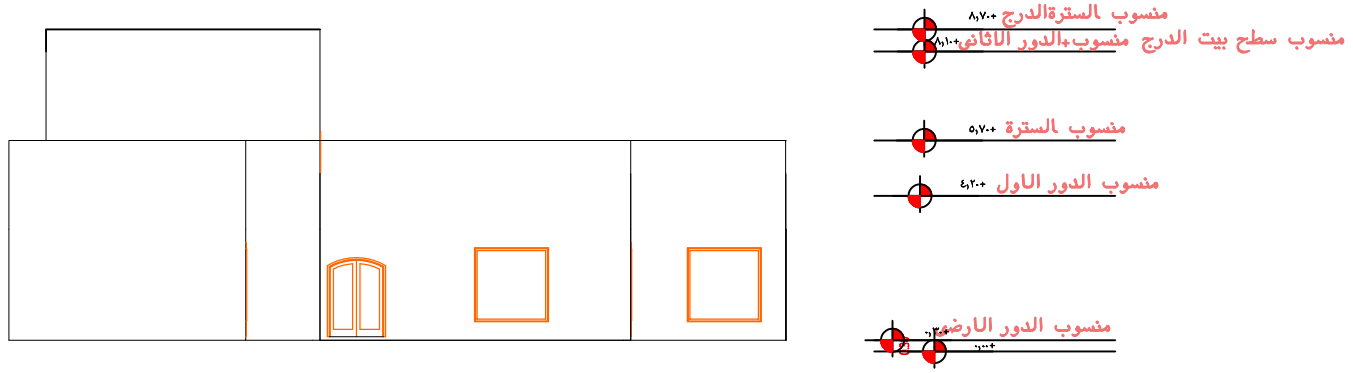

واجهة شرقية

بيانات خاصة بالموقع

الموقـــع	بلدية الرويضه		اتجاه الشمال
المنطقـــة	الرياض / طحى		
رقـــم القطعـــة	٥٠	رقم المخطط	١٧٩ الواقع بطحى
رقـــم الصـــك	٩٩٤٩٨٣٠٠٠٦٧٧	تاريـــخ الصـــك	١٤٤٦/١١/٣هـ
مساحة الارض بموجب التقرير المساحى	٦٣٠ م٢	رقـم اللوحة الجوية	
مساحة الارض بموجب التنظيم	٦٣٠ م٢	مساحة الارض بموجب الطبيعة	٦٣٠ م٢

2030

أمانة منطقة الرياض
RIYADH REGION MUNICIPALITY

ملاحظة:

- تم مراعاة تطبيق كود البناء السعودى فى تصميم المشروع
-(يعتمد على مسئولية المكتب الهندسى و متوافق مع كود البناء السعودى و مع الأنظمة و اللوائح المعتمدة التى تتطلبها وزارة النقل و الادارة العامة للدفاع المدنى ووزارة المياه و الكهرباء)
- تم اعداد مخططات العزل الحرارى للمبنى وفق متطلبات العزل الحرارى الواردةفى كود البناء السعودى

مكتب أحمد عبدالله العصيمي للاستشارات الهندسية
AHMED ABDULLAH ALOSAIMI
ENGINEERING CONSULTANT
ترخيص رقم : 6100003773

PROJECT: اسم المشروع : عمارة سكنية

LOCATION: الموقع : طحى

OWNER: المالك: تركى محمد ابن سويد العصيمى

المهندس الانشائى: احمدعبدالله العصيمى
عضوية هيئة المهندسين: رقم ٢٦٣٧٣١

المهندس المعمارى: مصطفى يوسف محمد احمد
عضوية هيئة المهندسين: رقم ٣٨٩٩٣٩

DRAWING OF: اسم اللوحة: الواجهات

مقياس الرسم: SCALE: 1:100

رقم اللوحة: DWG.N ٠٣

اعتماد المكتب:

التاريخ : DATE: ٢٨-٤-٢٠٢٥م

اتجاه الشمال

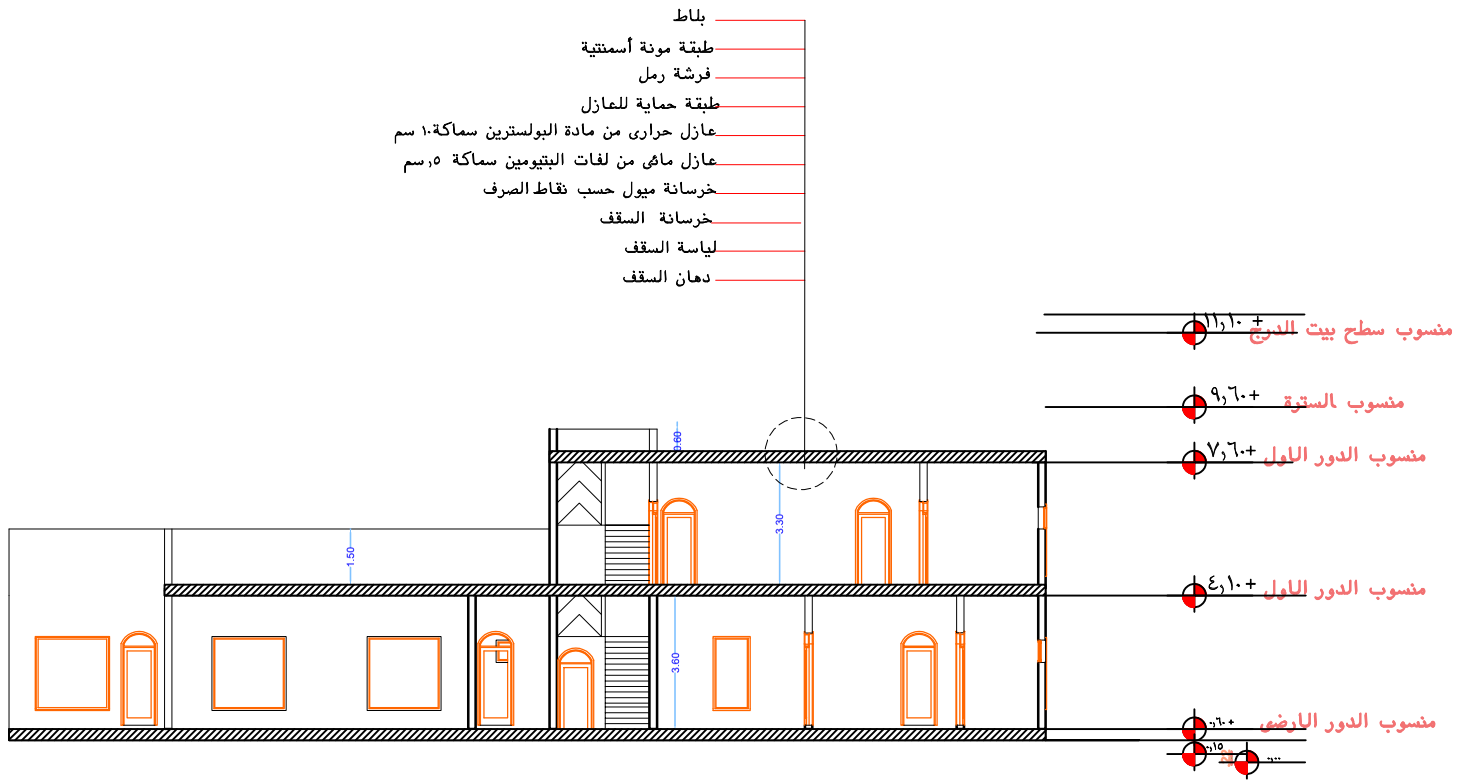

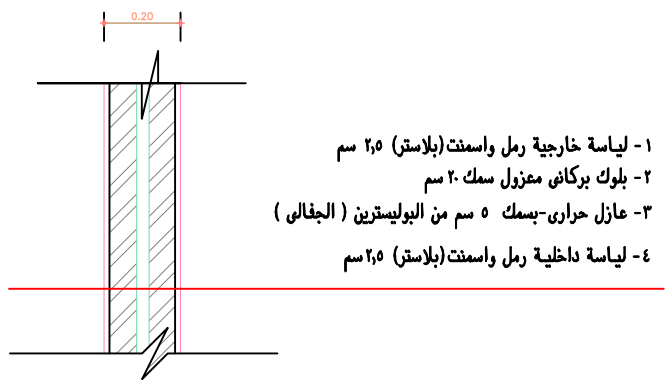

قطاع تفصيلى لعزل الحوائط الخارجية

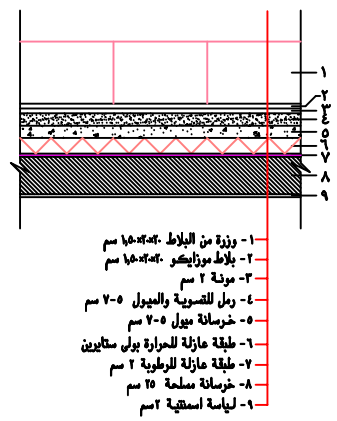

قطاع تفصيلى لعزل الاسقف

بيانات خاصة بالموقع

الموقع	بلدية الرويضه		اتجاه الشمال
المنطقة	الرياض / طحى		
رقم القطعة	٥٠	رقم المخطط	١٧٩ الواقع بطحى
رقم الصك	٦١٠٥٠٨٠٠٢٢٩١	تاريخ الصك	١٤٤٦/١١/٣هـ
مساحة الارض بموجب التقرير المساحى	٦٢٥,٥ م٢	رقم اللوحة الجوية	
مساحة الارض بموجب التنظيم	٦٢٥,٥ م٢	مساحة الارض بموجب الطبيعة	٦٢٥,٥م٢

2030

أمانة منطقة الرياض
RIYADH REGION MUNICIPALITY

ملاحظة:

- تم مراعاة تطبيق كود البناء السعودى فى تصميم المشروع
-(يعتمد على مسئولية المكتب الهندسى و متوافق مع كود البناء السعودى و مع الأنظمة و اللوائح المعتمدة التى تتطلبها وزارة النقل و الادارة العامة للدفاع المدنى ووزارة المياه و الكهرباء)
- تم اعداد مخططات العزل الحرارى للمبنى وفق متطلبات العزل الحرارى الواردةفى كود البناء السعودى

مكتب أحمد عبدالله العصيمي للاستشارات الهندسية
AHMED ABDULLAH ALOSAIMI
ENGINEERING CONSULTANT
ترخيص رقم : 5100003773
shg

PROJECT: اسم المشروع : عمارة سكنية

LOCATION: الموقع : طحى

OWNER: المالك: تركى محمد ابن سويد العصيمى

المهندس الانشائى: احمدعبدالله العصيمى
عضوية هيئة المهندسين: رقم ٢٦٣٧٣١

المهندس المعمارى: مصطفى يوسف محمد احمد
عضوية هيئة المهندسين: رقم ٣٨٩٩٣٩

DRAWING OF: اسم اللوحة: مسقط راسى ب

مقياس الرسم: SCALE: 1:100
رقم اللوحة: DWG.N ٠٣
التاريخ : DATE: ٢٨-٤-٢٠٢٥م
اعتماد المكتب: